

samuel de saboia


farol santander
rua joão brícola, 24 - centro histórico de são paulo,
são paulo - sp

LEGENDA

- EXPOGRAFIA A SER CONSTRUÍDA EM MDF
- BARRA SUSPensa DE FIXAÇÃO DOS PROJETORES FIXAS POR PRESSÃO NAS VIGAS
- OBRAS E INSTALAÇÕES
- PROJETOR
- INDICAÇÃO DE PINTURA

curador
antônio curti
prancha
planta 22º andar
escala
1:50
direção
felipe szutman
desenho
ss_expografia_ep-R02
revisão
arquiteta
brigida garrido


folha
01
04

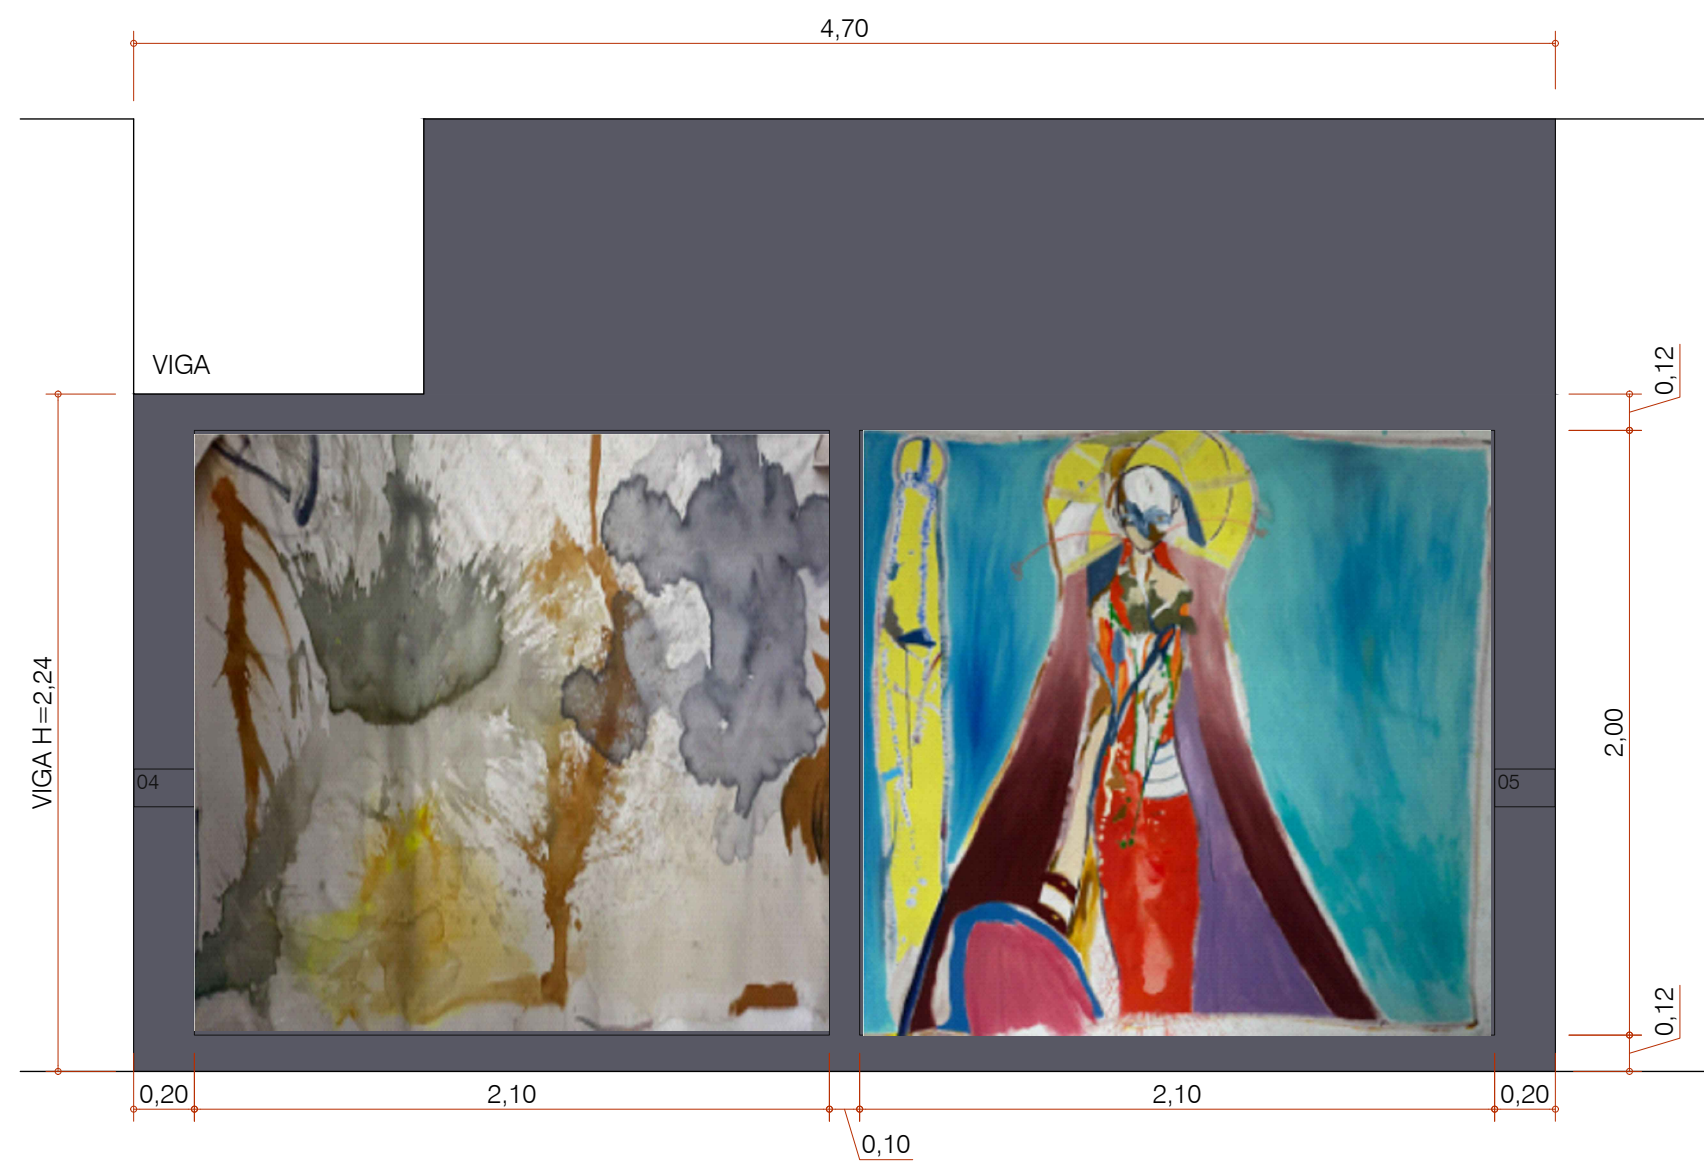

VISTA A
ESC 1:25



VISTA B
ESC 1:25

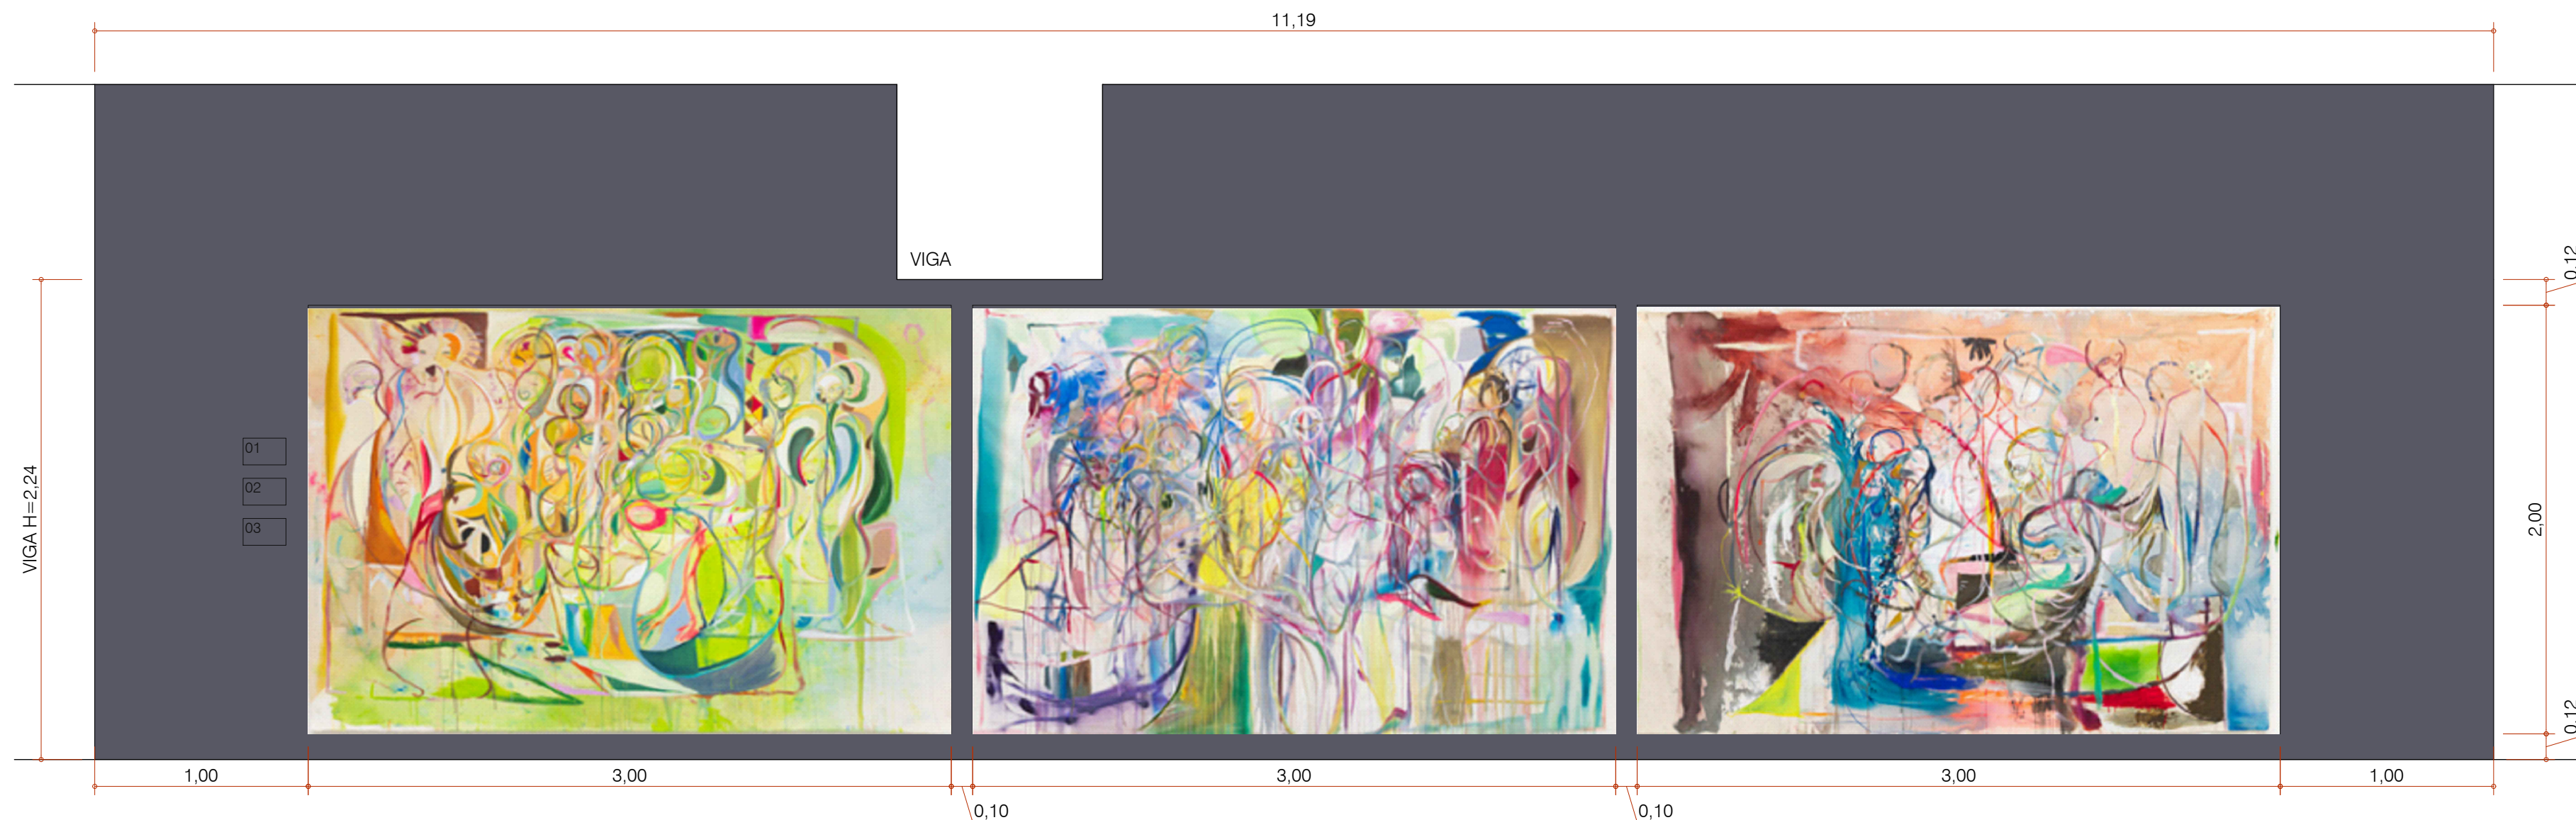

VISTA C
ESC 1:25

samuel de saboia

farol santander

rua joão brícola, 24 - centro histórico de são paulo,
são paulo - sp

curador
antônio curti
prancha
elevações
A | B | C
direção
felipe szutman


data
12.01.2025

desenho
ss_expografia_ep-R02
revisão

escala
1:25

arquiteta
brigida garrido

folha
02
04

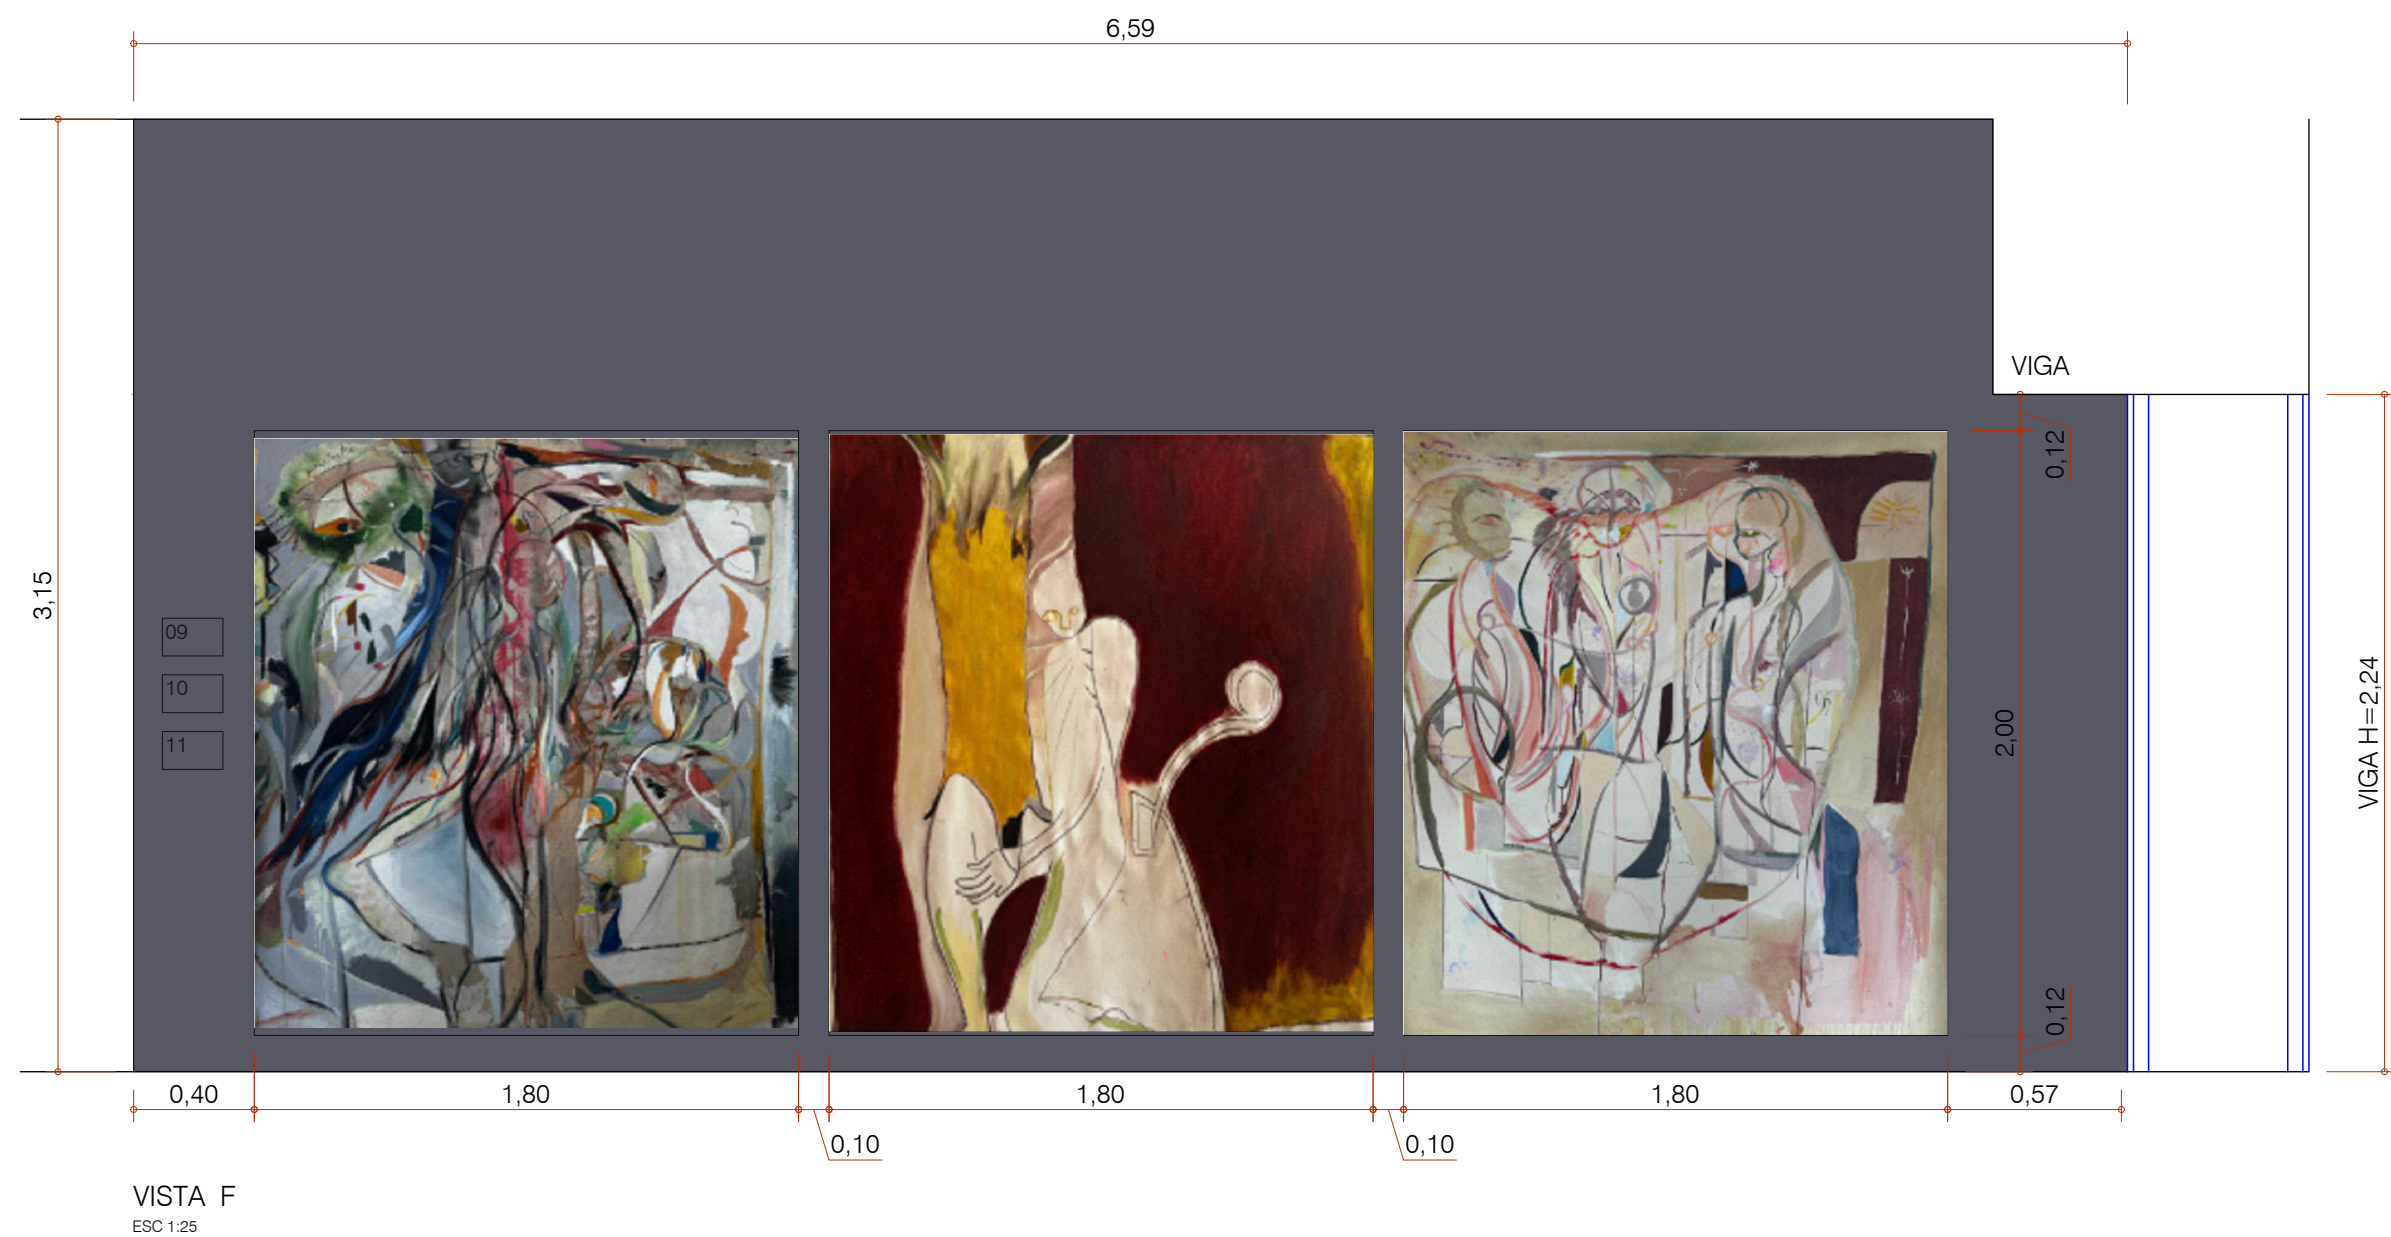

samuel de saboia

farol santander

rua joão brícola, 24 - centro histórico de são paulo,
são paulo - sp

curador

antônio curti

direção

felipe szutman

data

12.01.2025

desenho

ss_expografia_ep-R02

prancha

elevações
D|E|F|G

revisão

escala

1:25


arquiteta

brigida garrido


folha

03
04


BASE PARA INSTALAÇÃO DA
"MESA DO ARTISTA"
DUAS UNIDADES

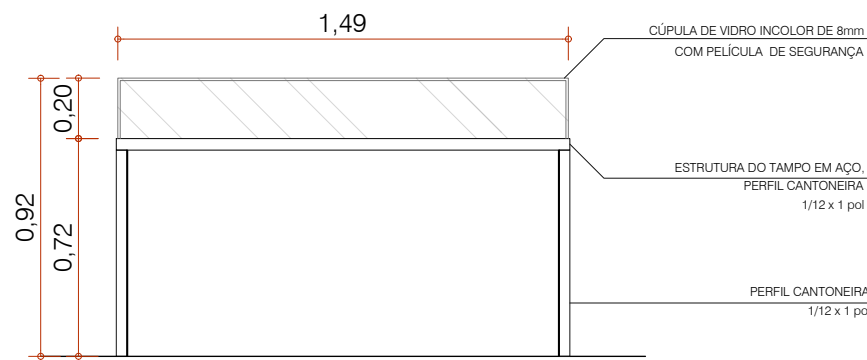


VISTA FRONTAL
ESC 1:25

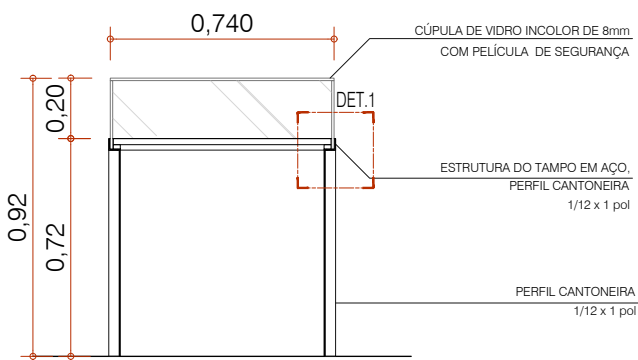


CORTE
ESC 1:25

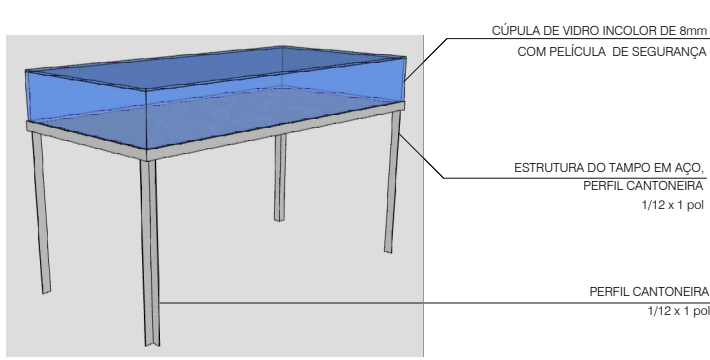


PERSPECTIVA
SEM ESCALA

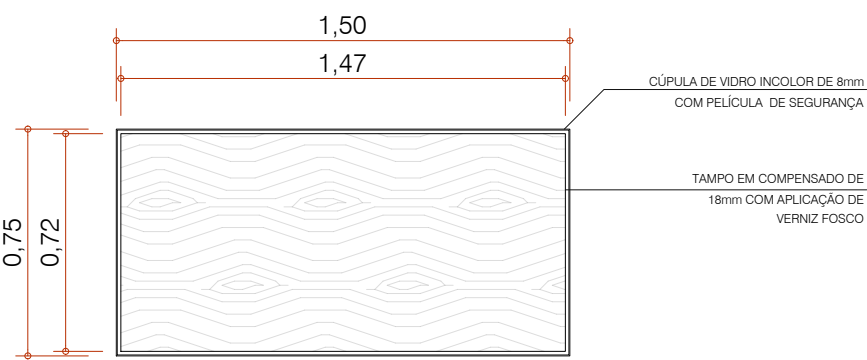


PLANTA BASE - SEM A CÚPULA
ESC 1:25

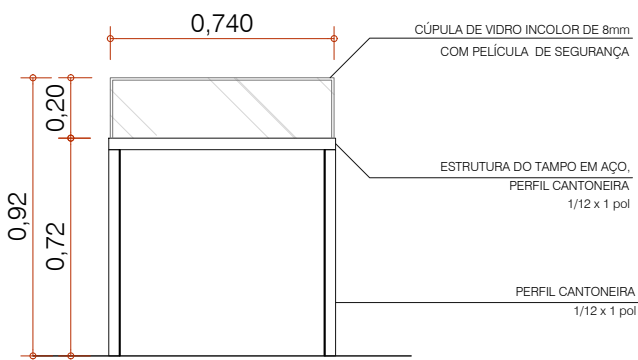

VISTA LATERAL
ESC 1:25

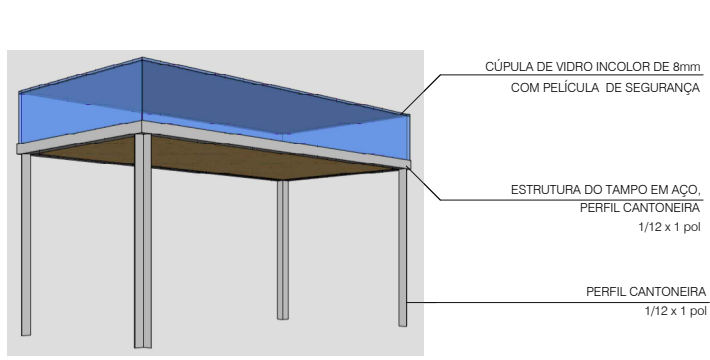


PERSPECTIVA
SEM ESCALA


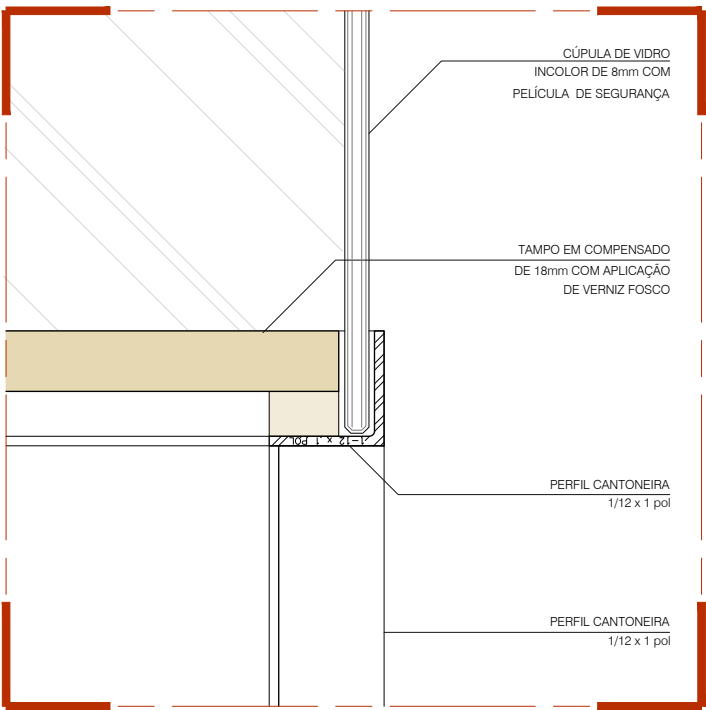


DETALHE 01
ESC 1:2,5



BANCOS EM MARCENARIA
TRÊS UNIDADES

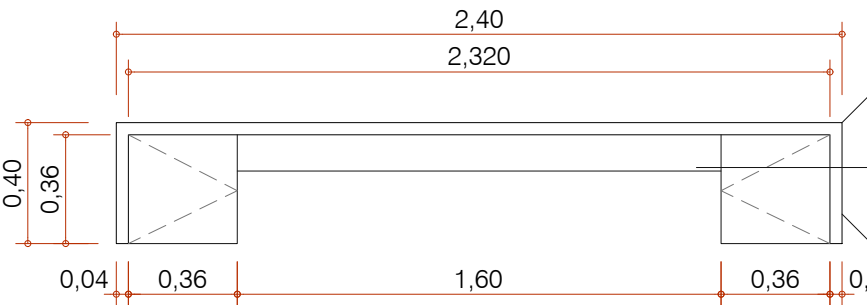

VISTA FRONTAL
ESC 1:25

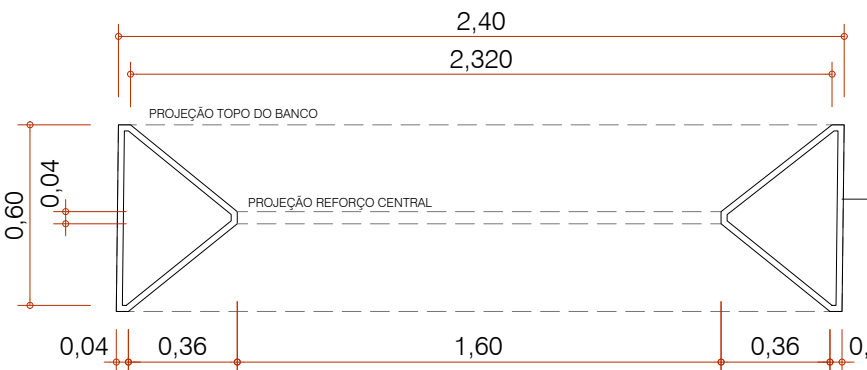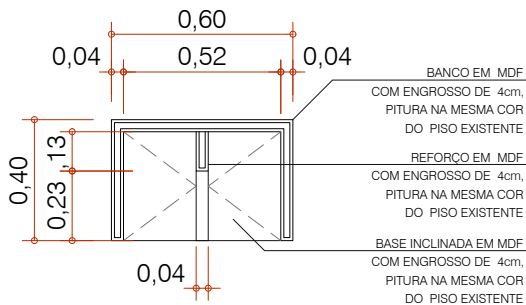

PLANTA BANCO - APOIO
ESC 1:25

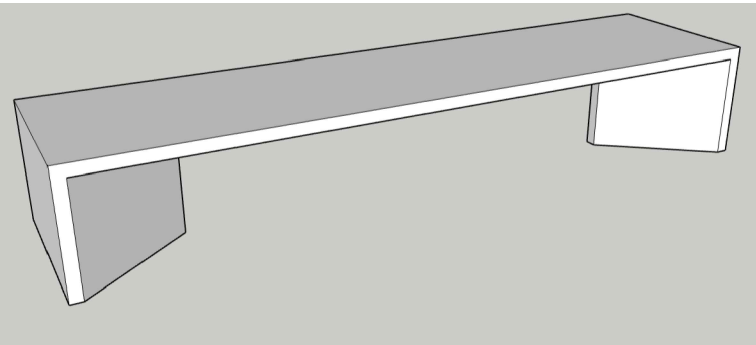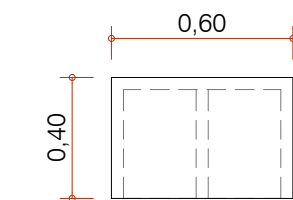

PERSPECTIVA
SEM ESCALA

samuel de saboia

farol santander
rua joão brícola, 24 - centro histórico de são paulo,
são paulo - sp

curador
antônio curti
prancha
detalhes
escala
1:25
direção
felipe sztutman
data
12.01.2025
desenho
ss_expografia_ep-R02
revisão
arquiteta
brigida garrido